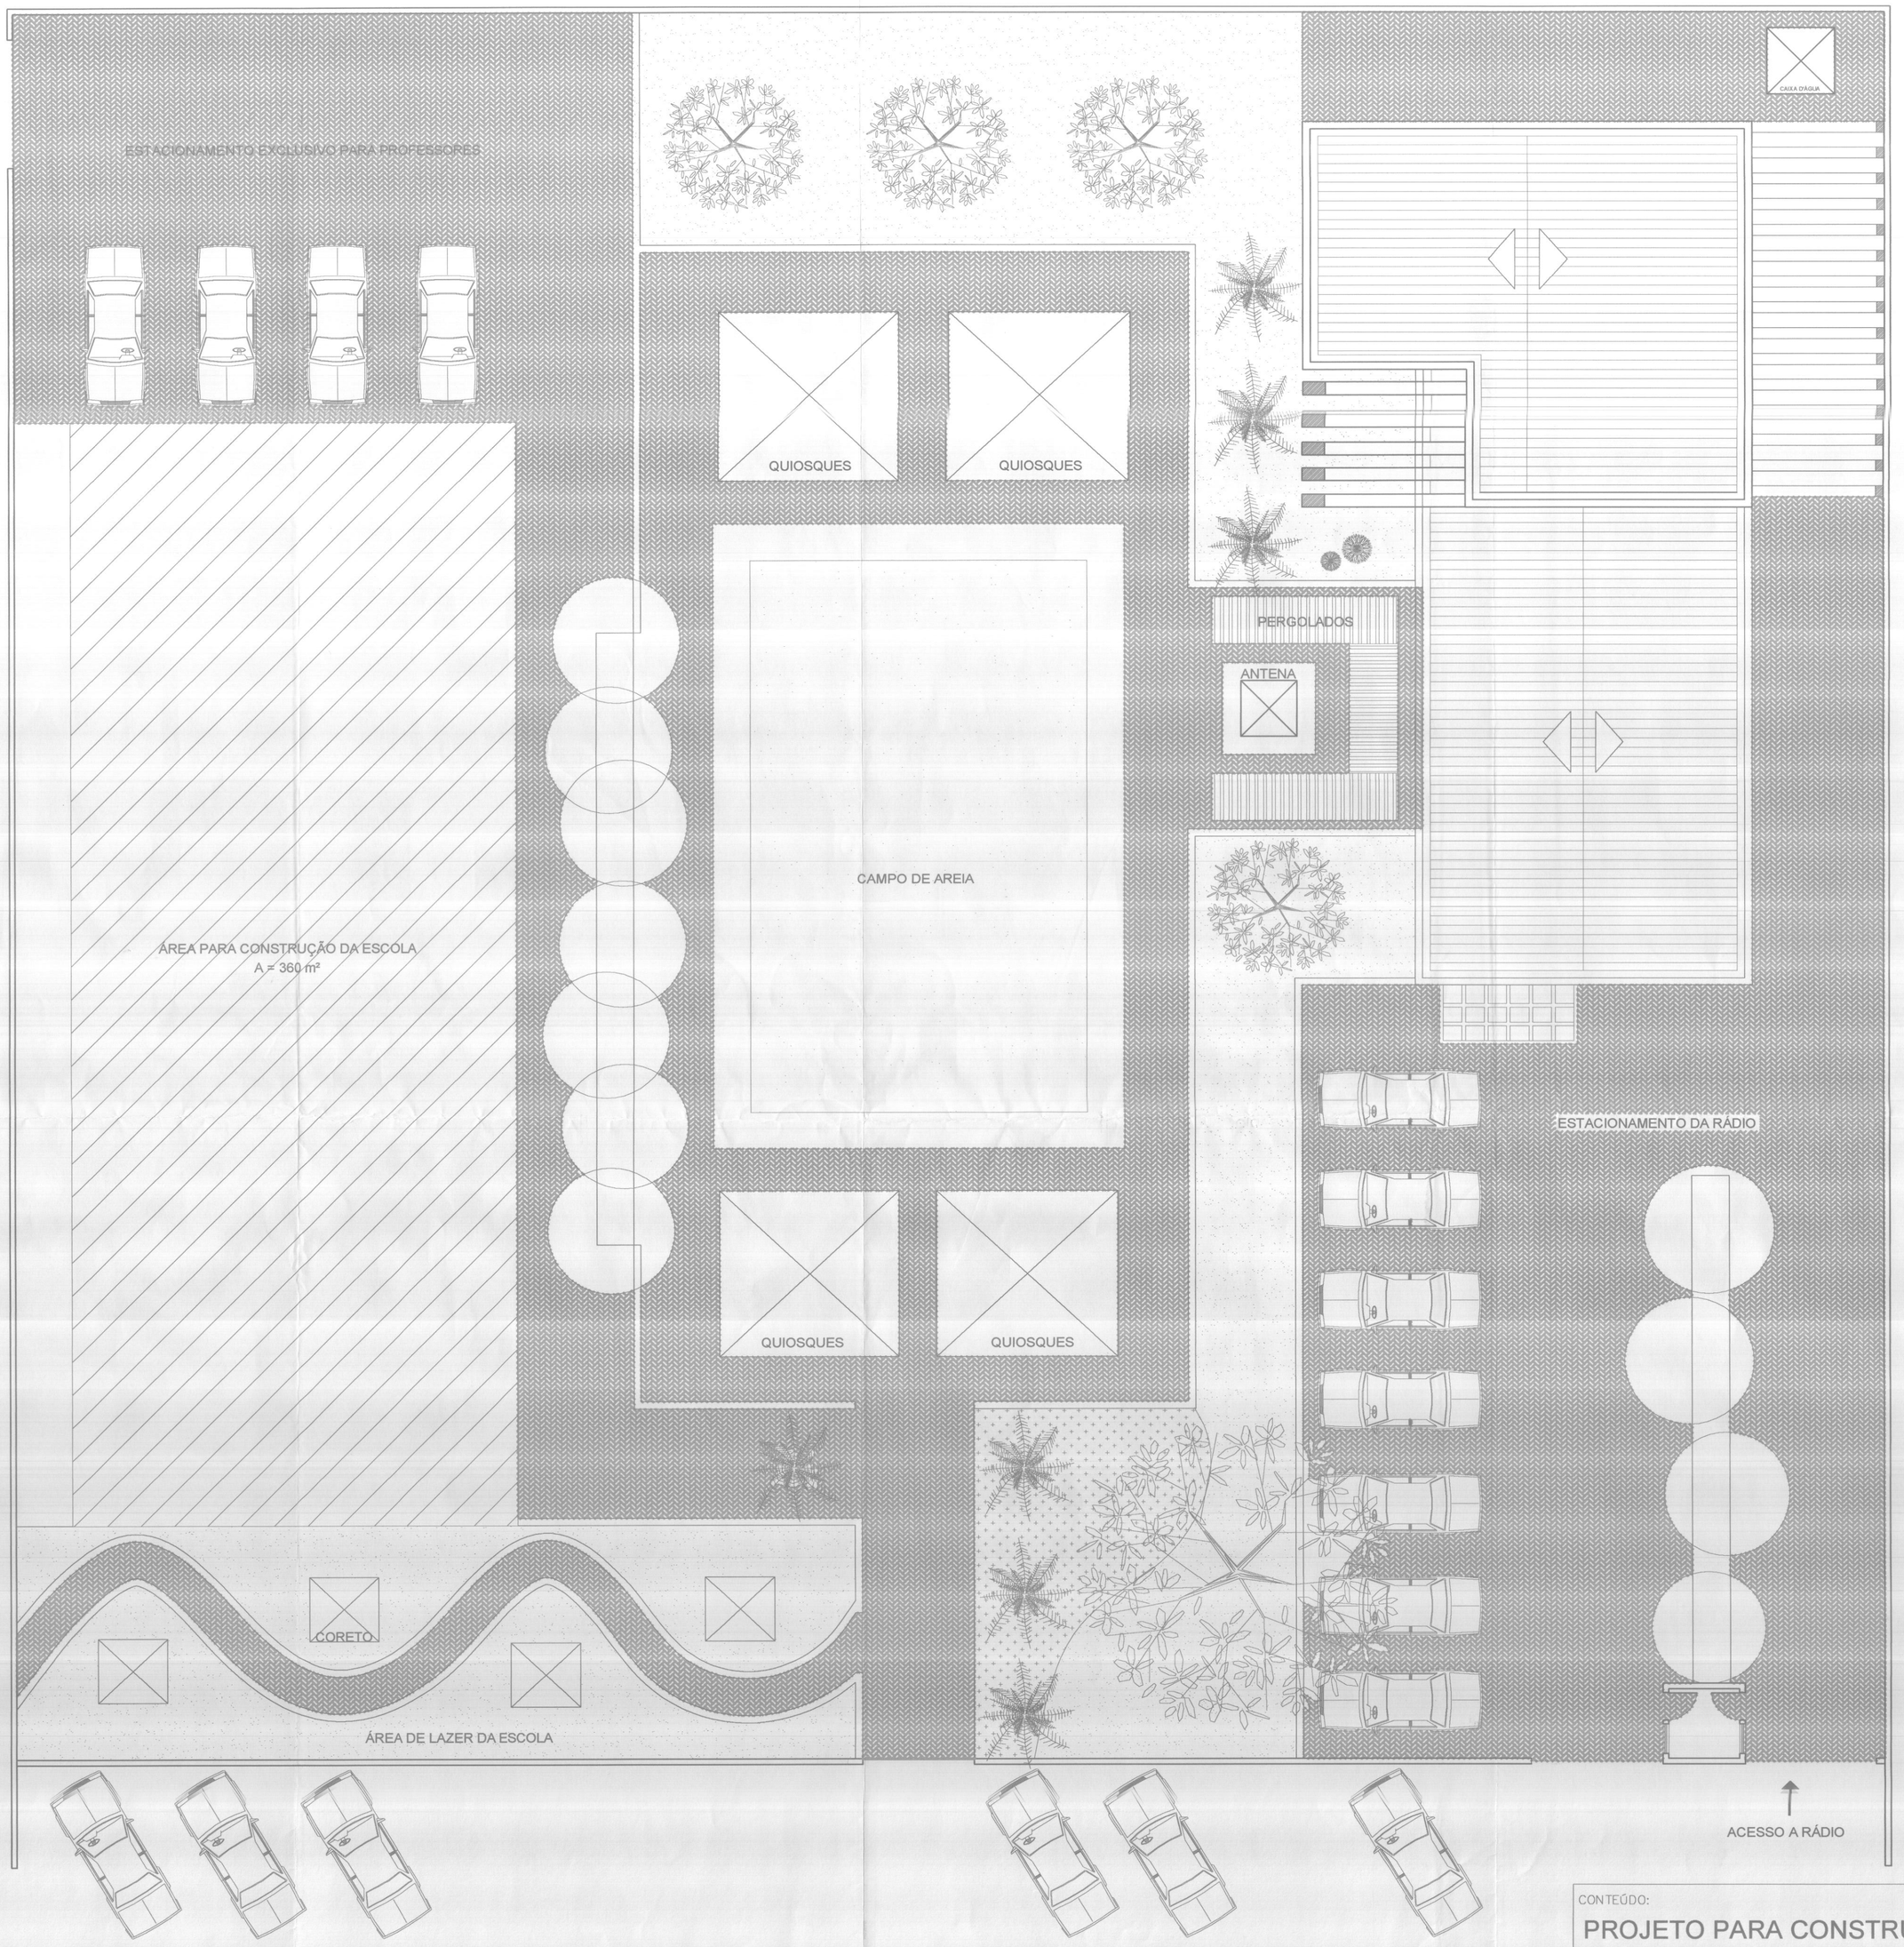

PLANTA DE LOCAÇÃO
ESC.1:75

Área do 2º Pavimento : 270.71m²

ECM - TECNOLOGIA E SOLUCOES LTDA:08505672000160

Assinado de forma digital por ECM - TECNOLOGIA E SOLUCOES LTDA:08505672000160
Dados: 2025.10.31 14:50:25 -03'00'

GOVERNO DO ESTADO DO AMAPÁ
FLS. 27
PROC.
IMAP

AUTOR DO PROJETO:

Arq. ISABELLA SUSSUARANA

PROPRIETÁRIO: FUNDAÇÃO CULTURAL E ASSISTÊNCIAL ÁGUA VIVA

CONTEÚDO:

PROJETO PARA CONSTRUÇÃO DE UMA ÁREA MULTIUSO
PLANTA BAIXA,COBERTURA, FACHADA, CORTES 01 E 02

PROJETO: ARQUITETÔNICO

ÁREA DO TERRENO:	ESCALA:	DATA:	PRANCHA Nº:
2.522,54²	INDICADA	NOVEMBRO/2012	01/05
ÁREA DE CONSTRUÇÃO: 312,58m²	ÁREA DE INTERVENÇÃO:	DES./CAD. Isabella Sussuarana	